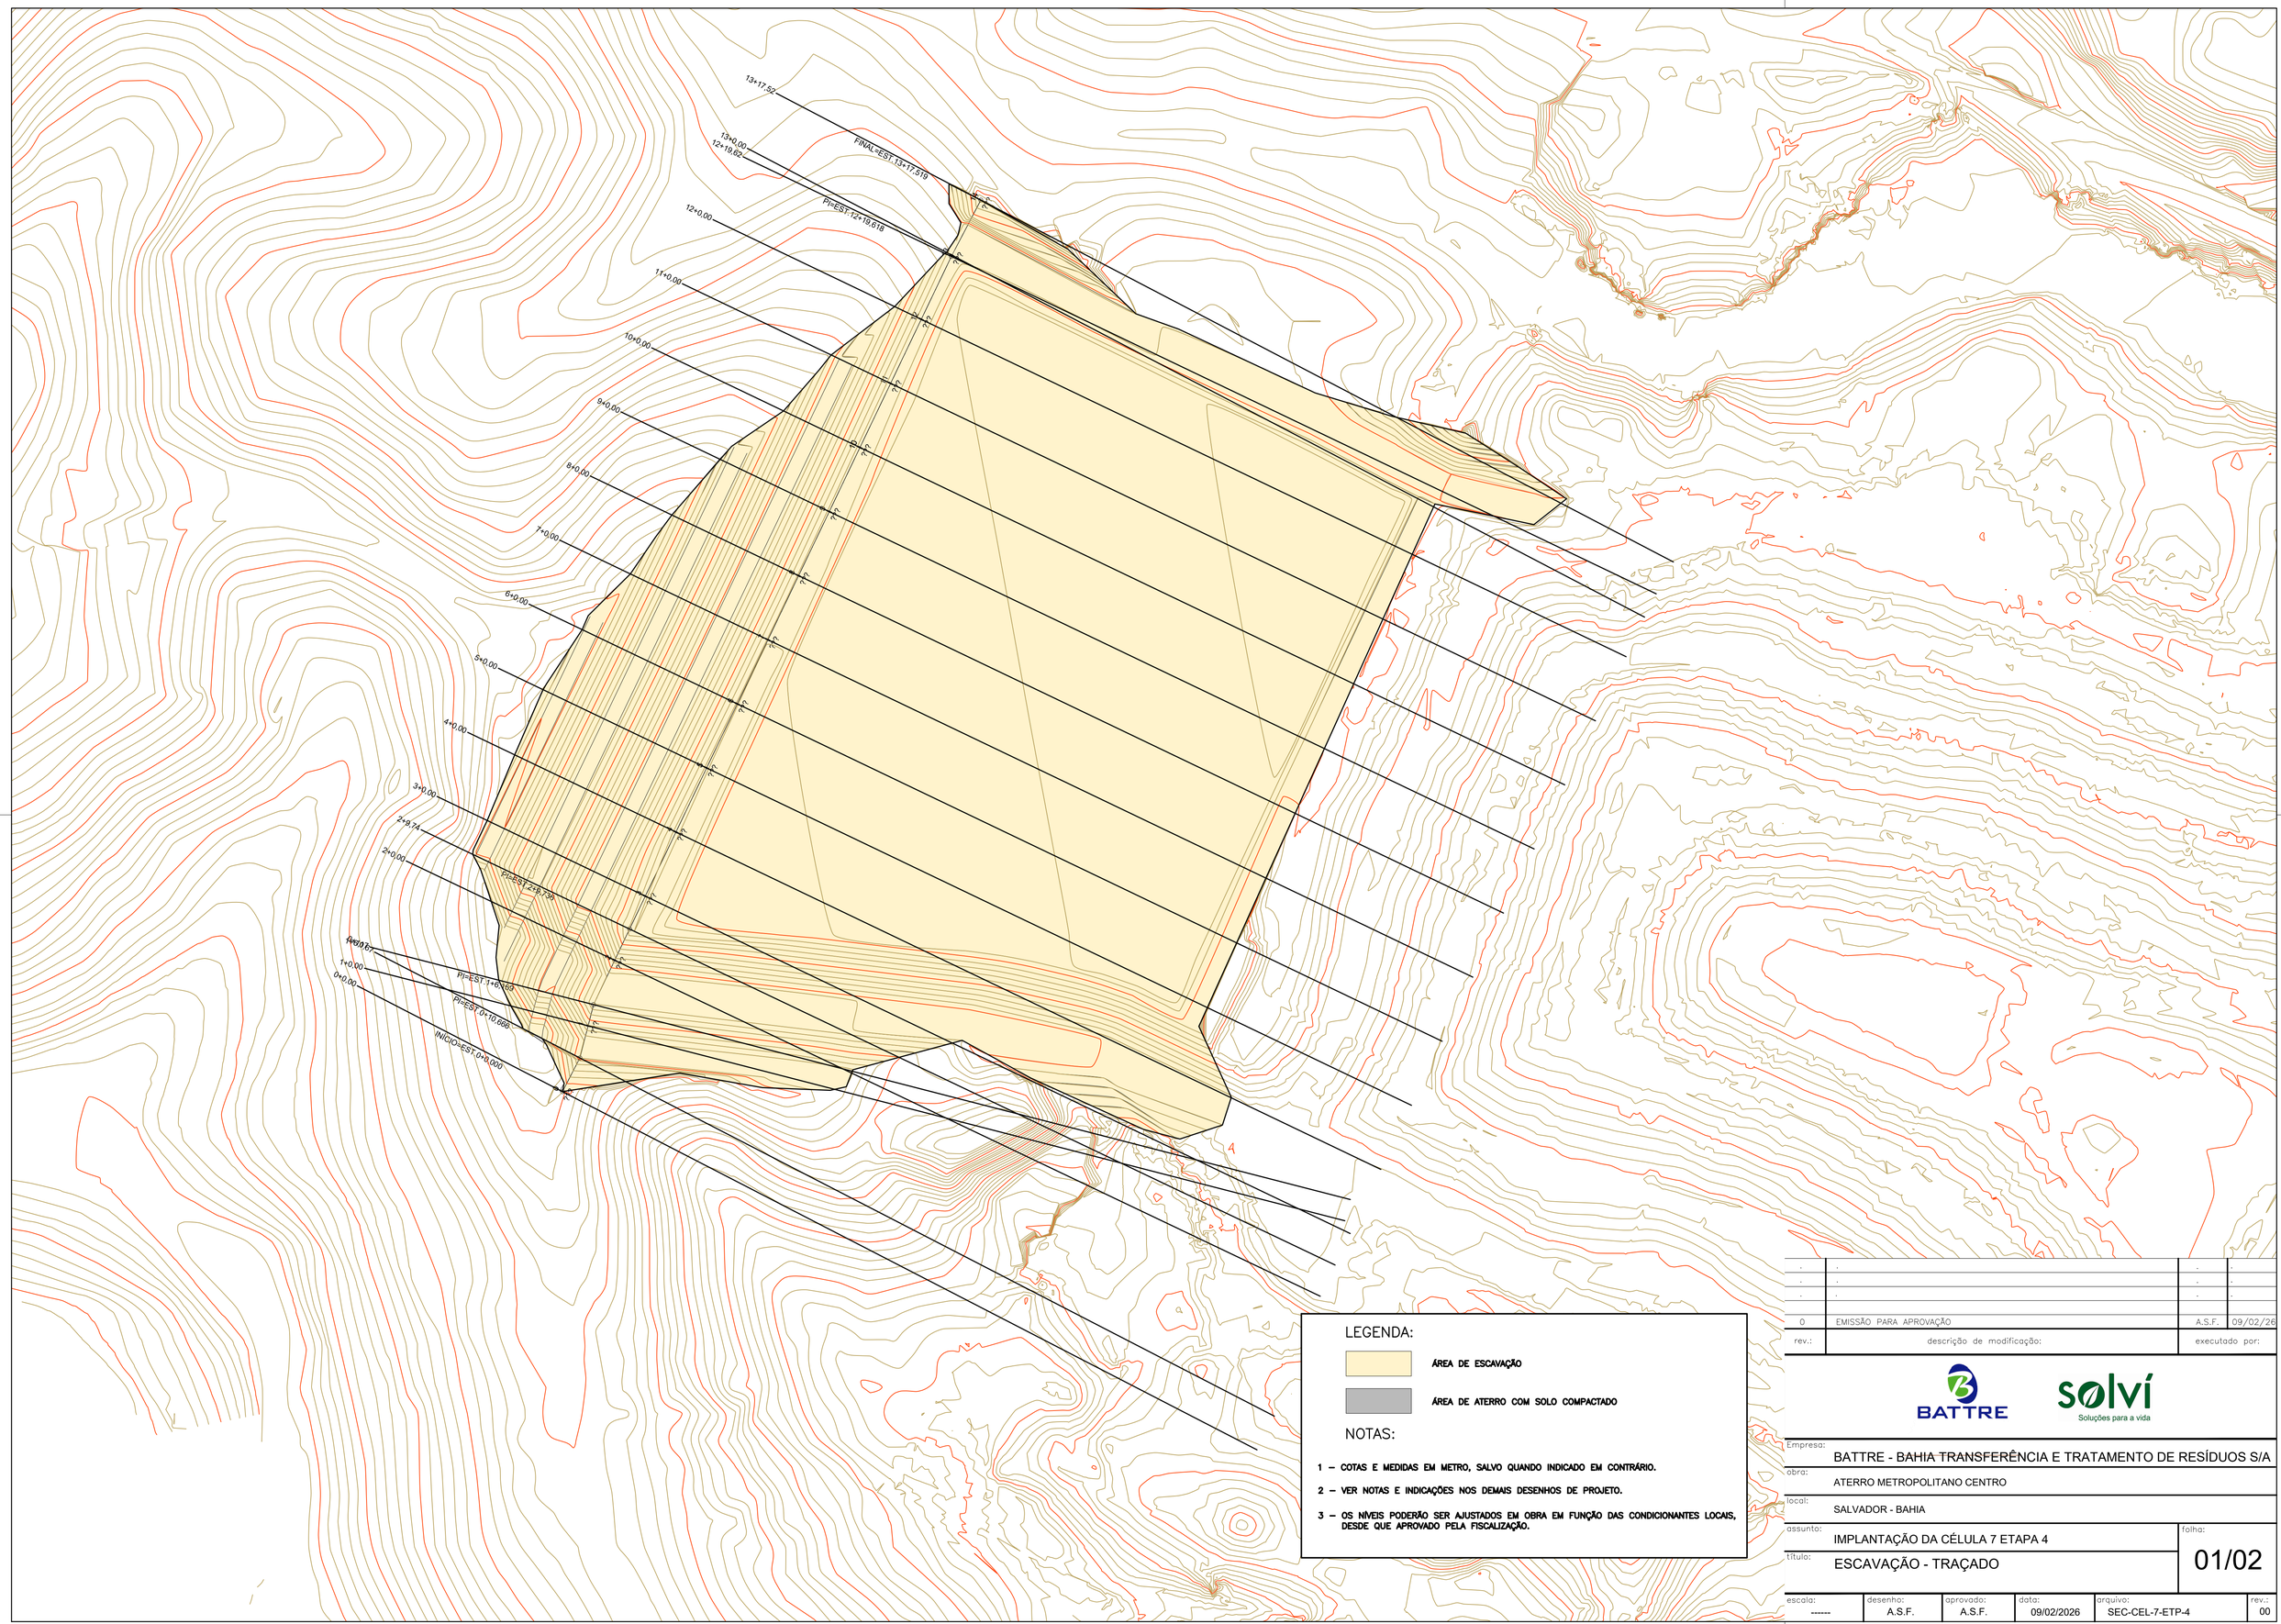


LEGENDA:

ÁREA DE ESCAVAÇÃO

ÁREA DE ATERRO COM SOLO COMPACTADO

NOTAS:

1 – COTAS E MEDIDAS EM METRO, SALVO QUANDO INDICADO EM CONTRÁRIO.

2 – VER NOTAS E INDICAÇÕES NOS DEMAIS DESENHOS DE PROJETO.

3 – OS NÍVEIS PODERÃO SER AJUSTADOS EM OBRA EM FUNÇÃO DAS CONDICIONANTES LOCAIS, DESDE QUE APROVADO PELA FISCALIZAÇÃO.

rev.:	descrição de modificação:	executado por:	
.	.	.	.
.	.	.	.
.	.	.	.
0	EMISSÃO PARA APROVAÇÃO	A.S.F.	09/02/26

BATTRE

solví
Soluções para a vida

empresa:	BATTRE - BAHIA TRANSFERÊNCIA E TRATAMENTO DE RESÍDUOS S/A
obra:	ATERRO METROPOLITANO CENTRO
local:	SALVADOR - BAHIA
assunto:	IMPLANTAÇÃO DA CÉLULA 7 ETAPA 4
título:	ESCAVAÇÃO - TRAÇADO
folha:	01/02

escala:	desenho:	aprovado:	data:	arquivo:	rev.:
------	A.S.F.	A.S.F.	09/02/2026	SEC-CEL-7-ETP-4	00